


Pillar of Study


Vanderbilt University is one of the **most historic and prestigious research universities** in the nation. Renowned for its rigorous academics, distinguished faculty, and picturesque campus,

the new residential design aims to embody the university's rich history and values. To achieve this, the residence features an **entry portal that serves as a symbolic 'Pillar of Studies,'**

representing the **transition from the vibrant energy of student life to a more reflective, restful, and didactic environment.**

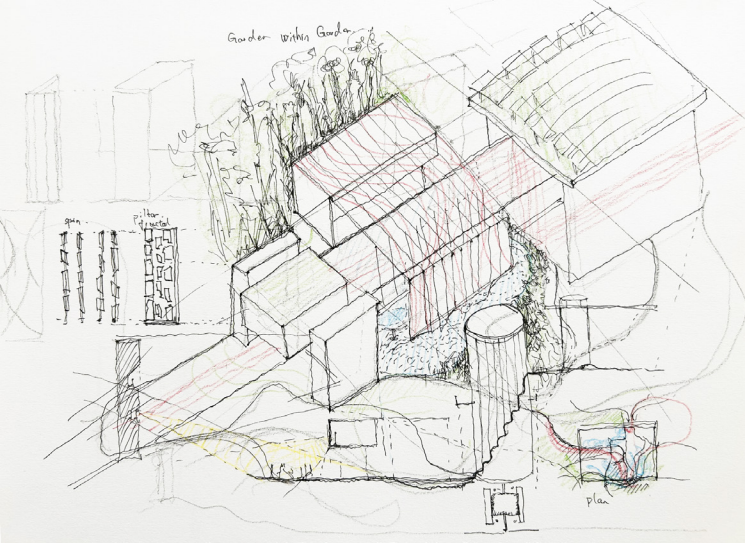


Design Comic - Garden within a Garden

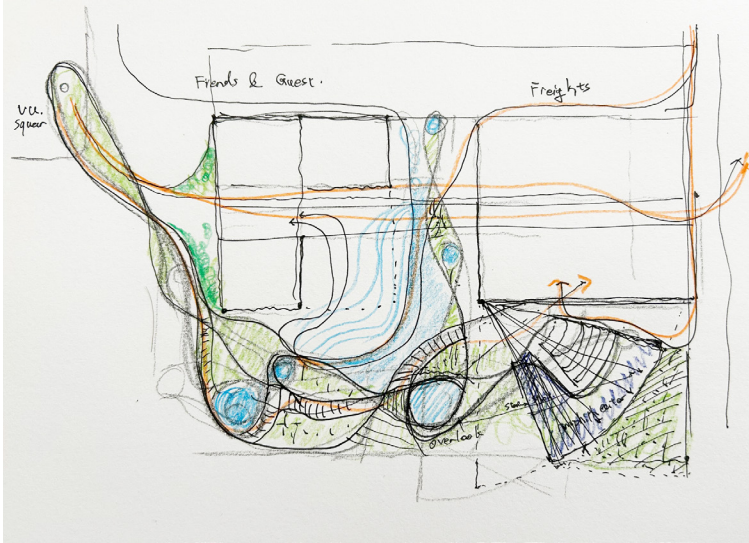

Design Comic - Site Strategy



Entry Portal

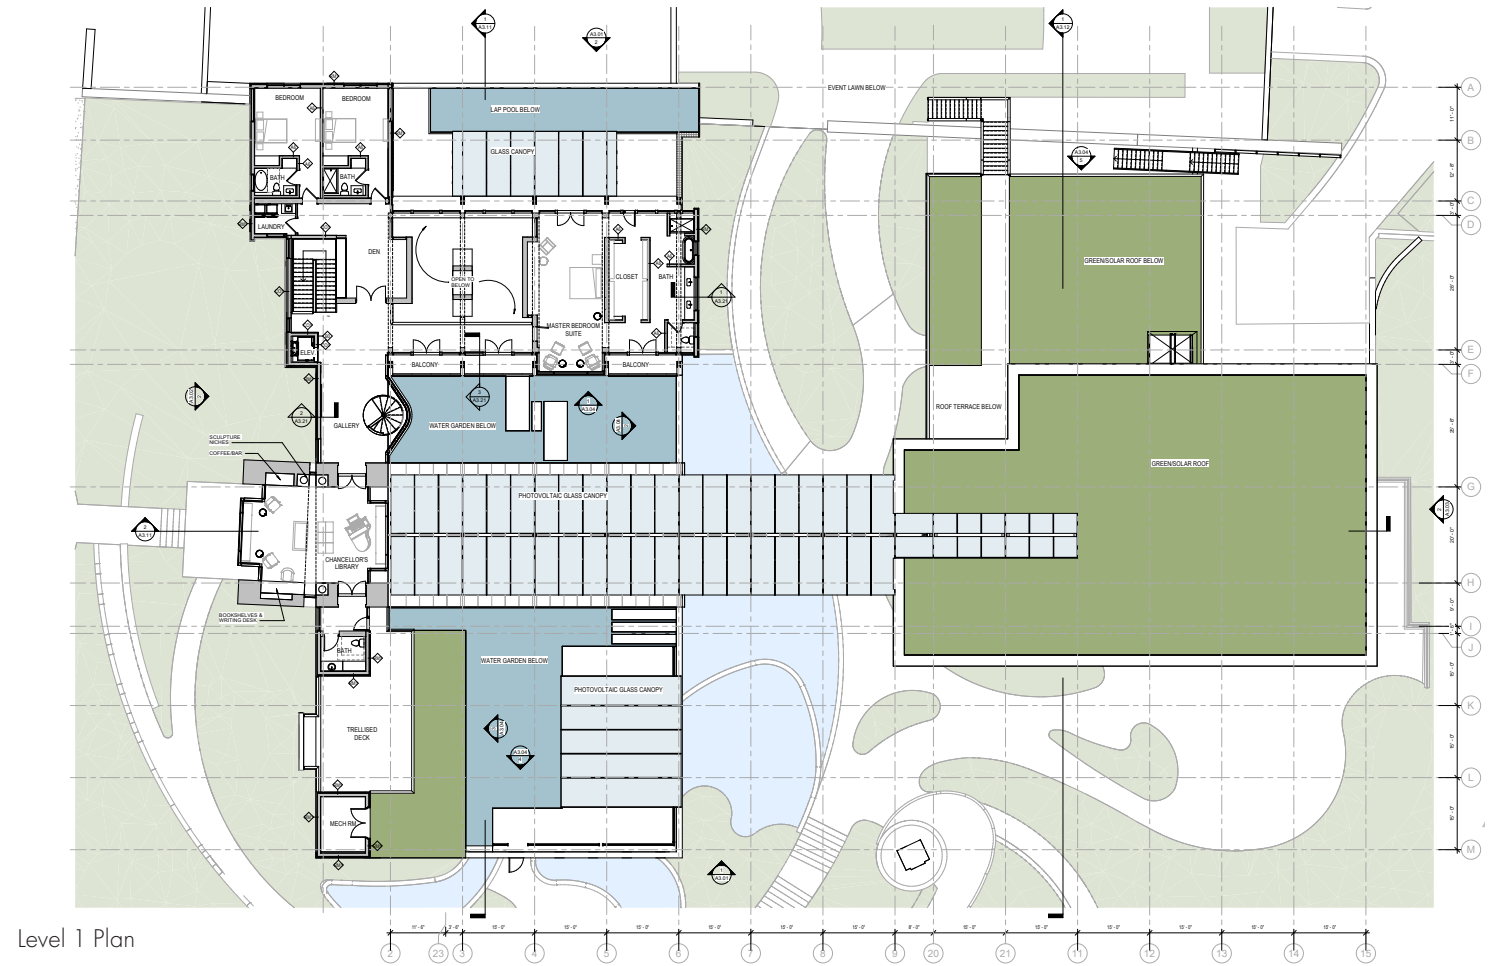

Level 1 Plan



Arbor in Inner Garden