


Respecting Existing and Looking to the Future

The materiality of the project bridges **historic craftsmanship and contemporary expression**. The existing church, built in the Gothic style, features locally sourced Sewanee sandstone and Bowling Green stone, with finely carved detailing and a pronounced water table that

grounds the structure. The new addition draws from these defining elements—**mirroring the height, proportions, and subtle projections**—while introducing refined aluminum and steel components. Its **exterior features precision water jet-cut panels, crafted with intricate**

patterns that filter light in shifting patterns throughout the day. Metaphorically, the addition becomes a **lantern—symbolizing the church as the glowing heart of its worshippers**—radiating warmth and welcome while harmonizing with the enduring strength of the original masonry.

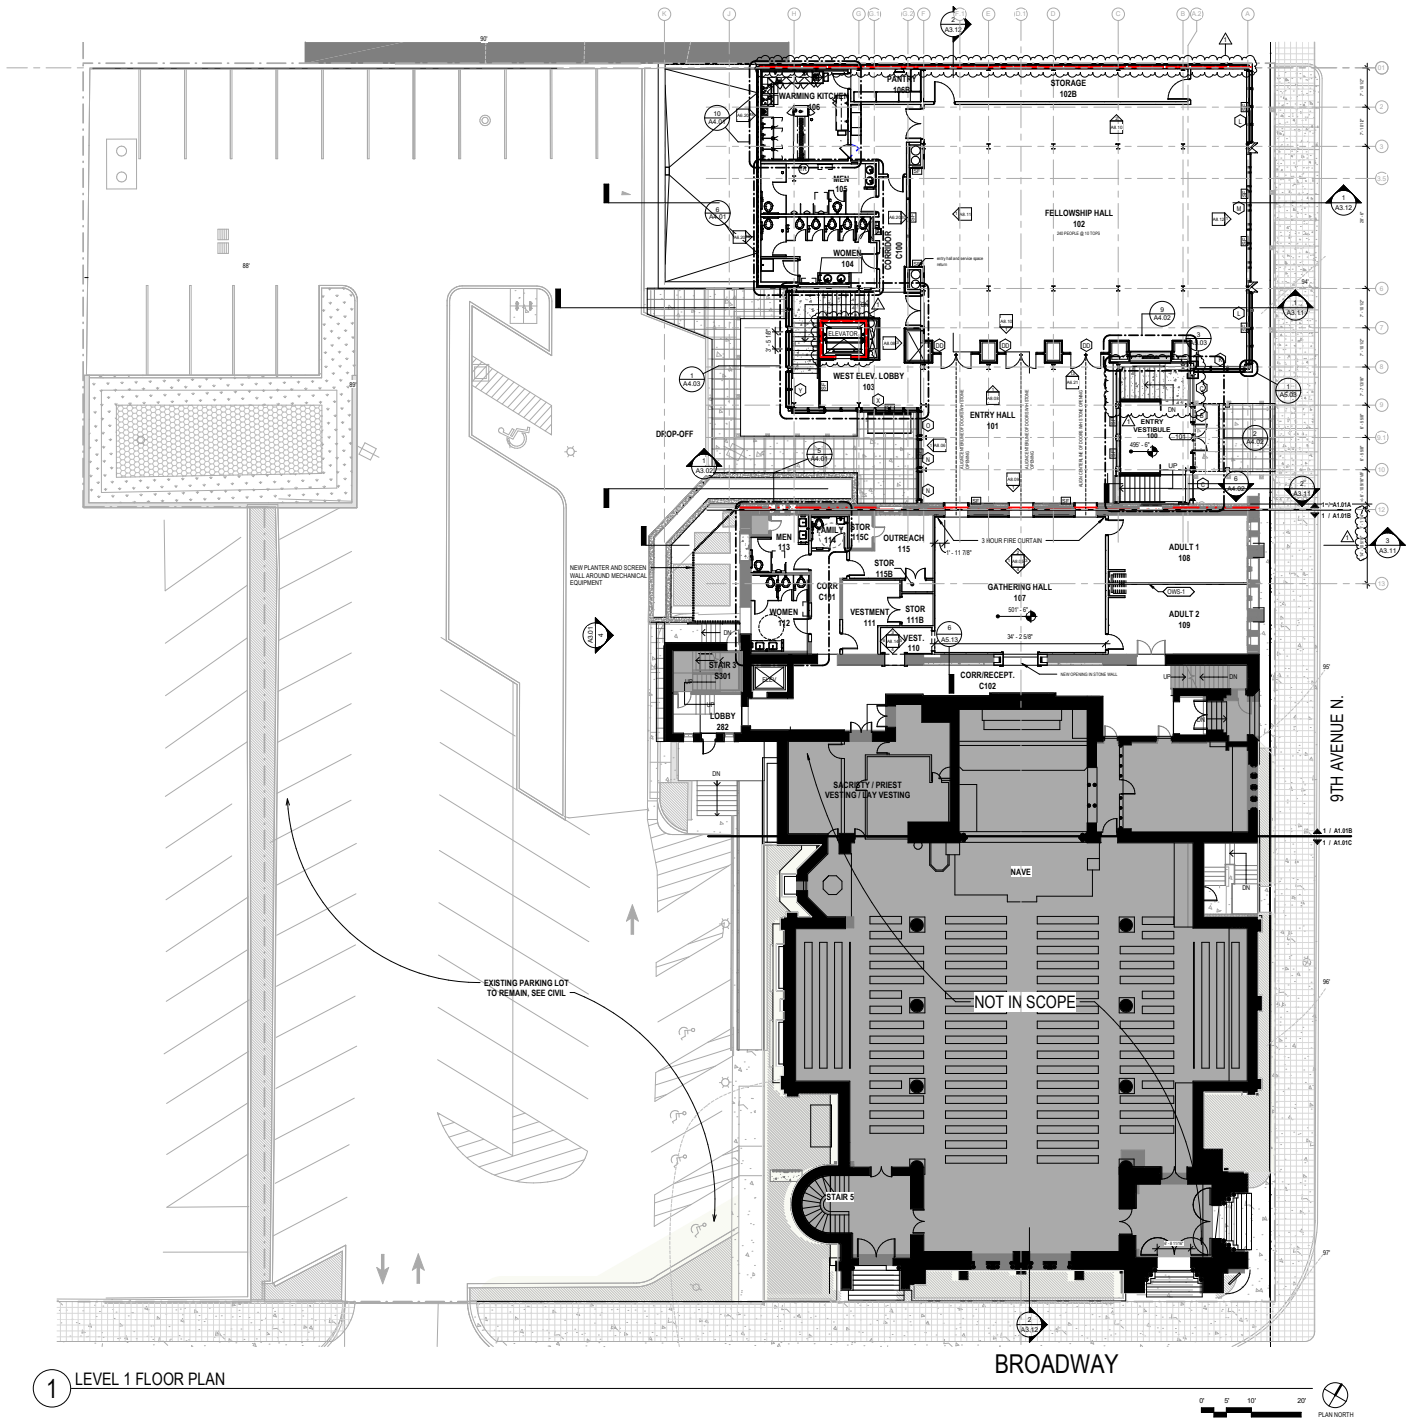

Christ Church Cathedral as a Lantern - Filtering Light and Preaching the Gospel

